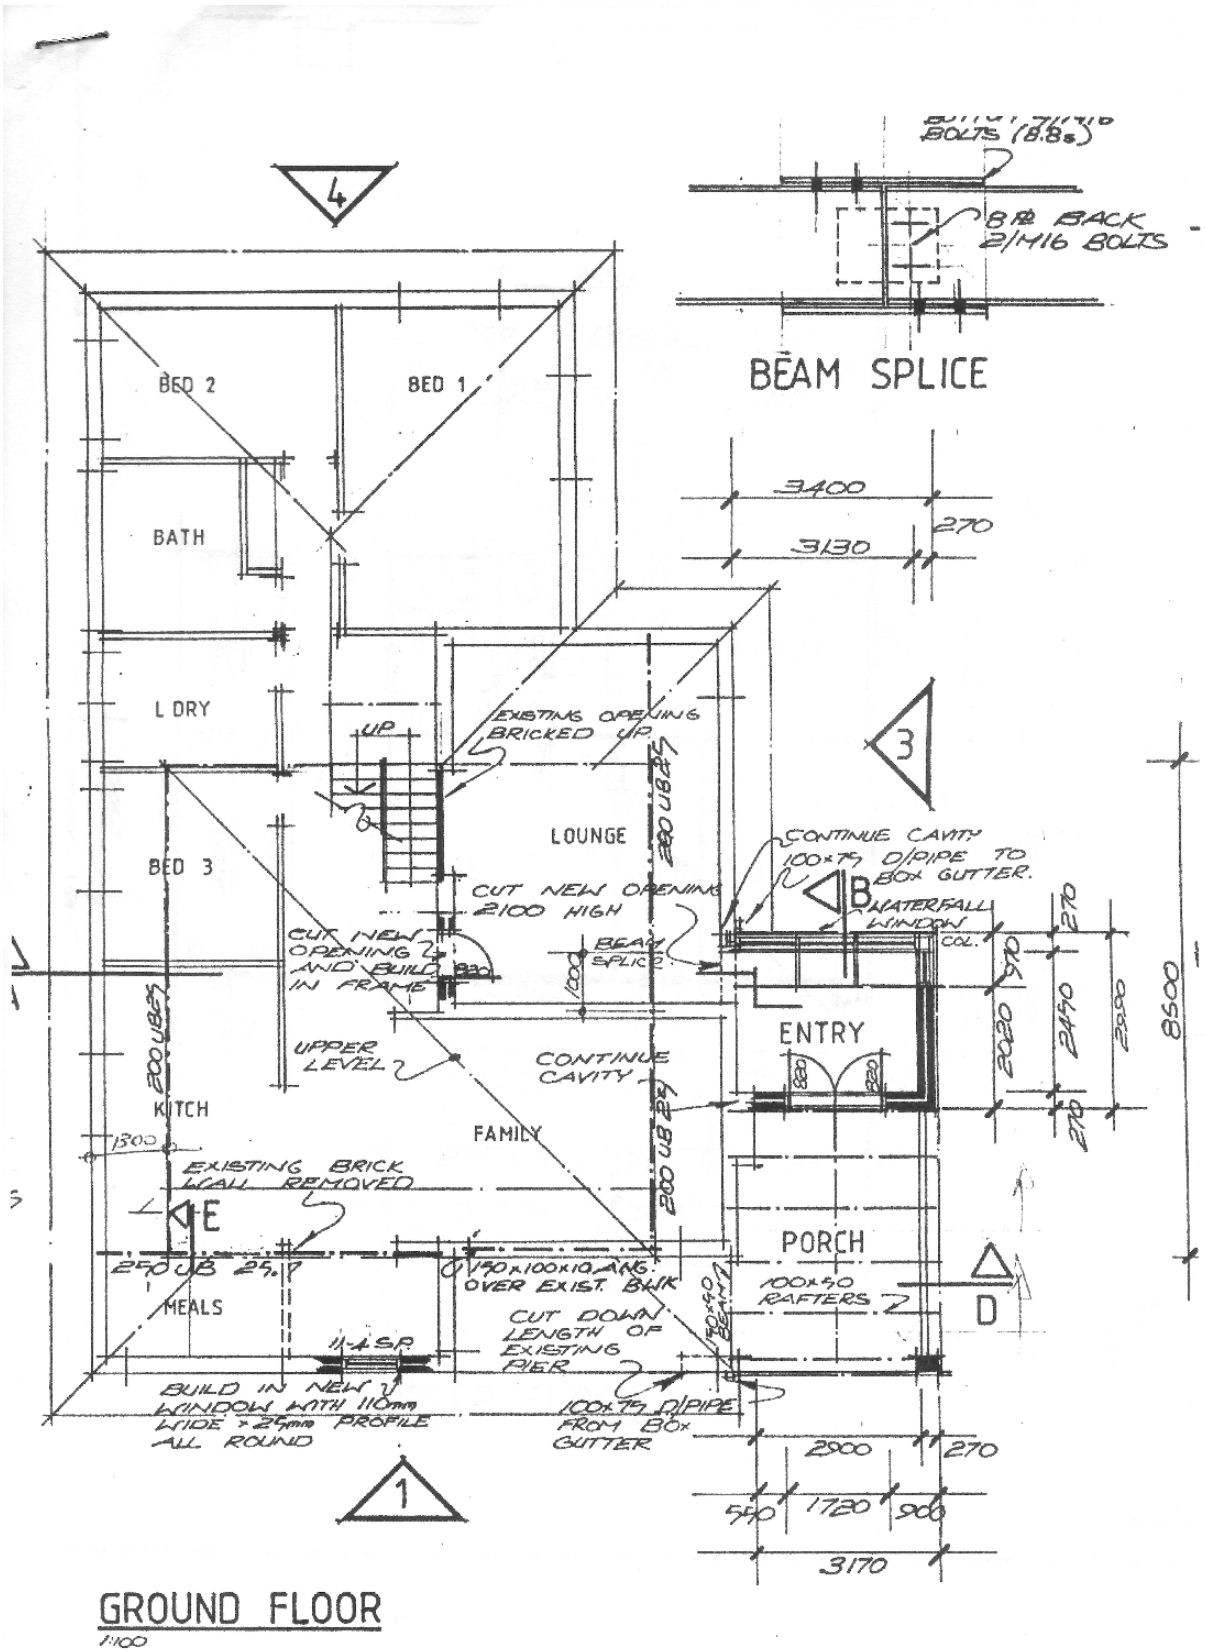


GROUND FLOOR

1:100